
Floor plan, 1:50. Metres in the plan; dimensions in millimetres. The street at the left; the bar along the top wall. A proposal: every number is a working assumption (README, "Assumptions") for the owner to overturn.

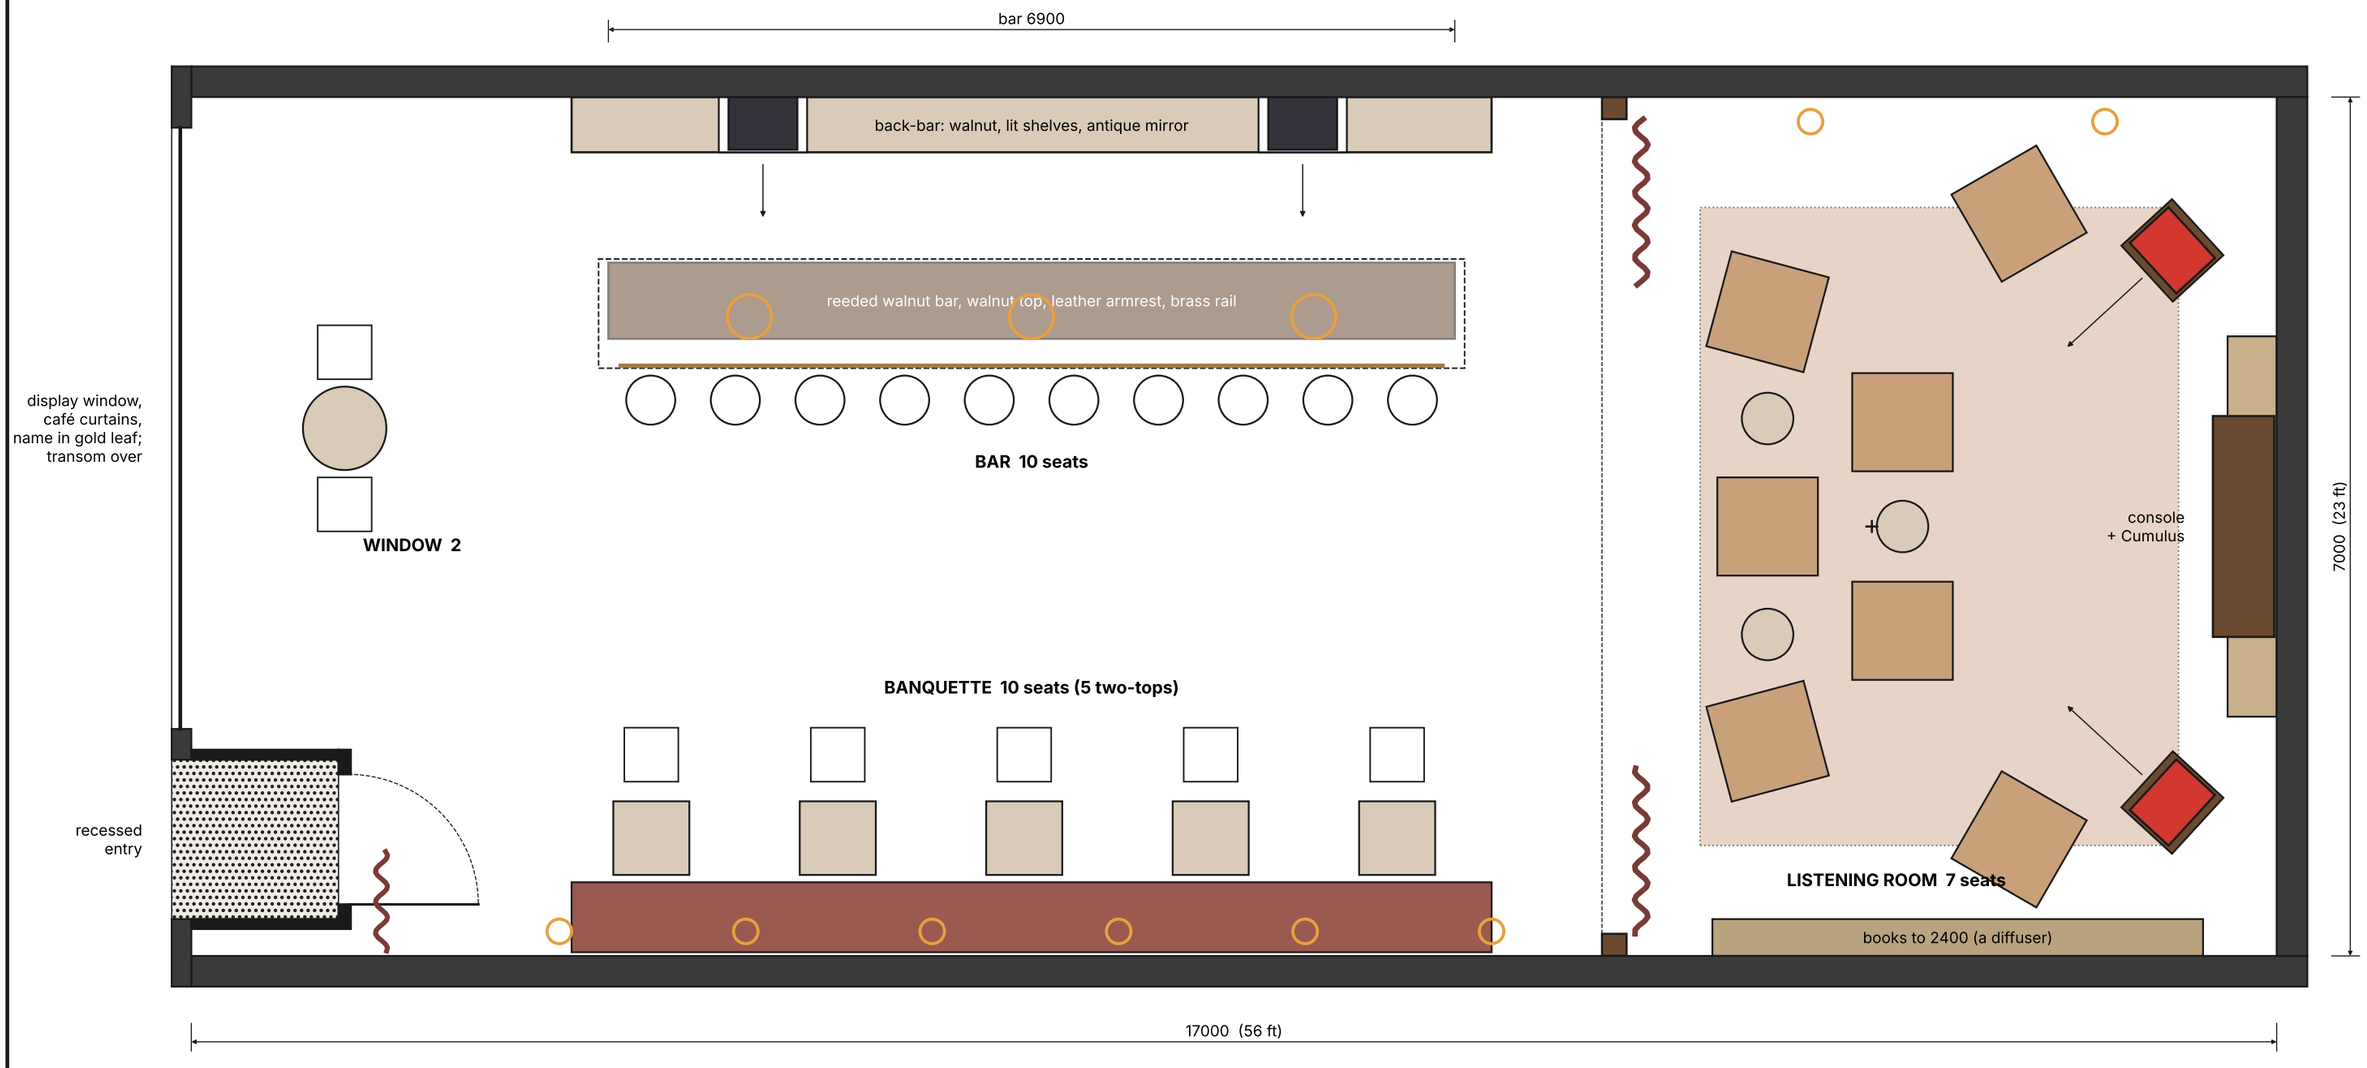

29 seats; occupant load 40 (Group B, under 50)

Acoustic treatment

- oxblood wool velvet: the door curtain and the listening room's curtains (drawn, they close it off)
- books, floor to 2400, 300 deep: a diffuser on the listening room's right wall
- the record wall: cubbies of LPs 400 deep, to 2700, a diffuser
- listening room ceiling: walnut slats 45 at 90 over 50 black absorber
- a wool rug under the chairs; leather and velvet throughout
- the banquette: oxblood leather, channel-tufted

Products

Atmosphere: the Ember pair either side of the record wall on low walnut plinths, each aimed at the listening seat (+); the Smoke pair in the back-bar's two niches, floor 450, the horns at a stool's eye. Arrows: each speaker's axis. Bell (Dust): table lamps. Cumulus: a small stand-in on the console while the companions are redesigned.

Light (warm, 2200 to 2700 K), in pools

circles in amber: shaded brass sconces at 1720 (six on the right wall, two on the brick); three spun-brass pendants over the bar, rims 800 over the top; the back-bar's shelves lit from strips under their front edges; a pinhole in each niche; Bell (Dust) on two two-tops, the window table and two lounge tables; candles on the rest; a picture light under the record wall's cornice; a soft lamp over each Ember speaker.


Floor plan

Planet EARF: Listening bar, San Francisco (a proposal, round 33)

mm | issue 2026-10-19 | first angle

Set out from the shell's inside faces; joinery to +-2, the shell +-10

Long section A-A, 1:50, cut along the room 3930 from the right-hand wall, looking at the bar wall: what is cut is drawn heavy, what lies beyond light.
Heights in millimetres above the finished floor.

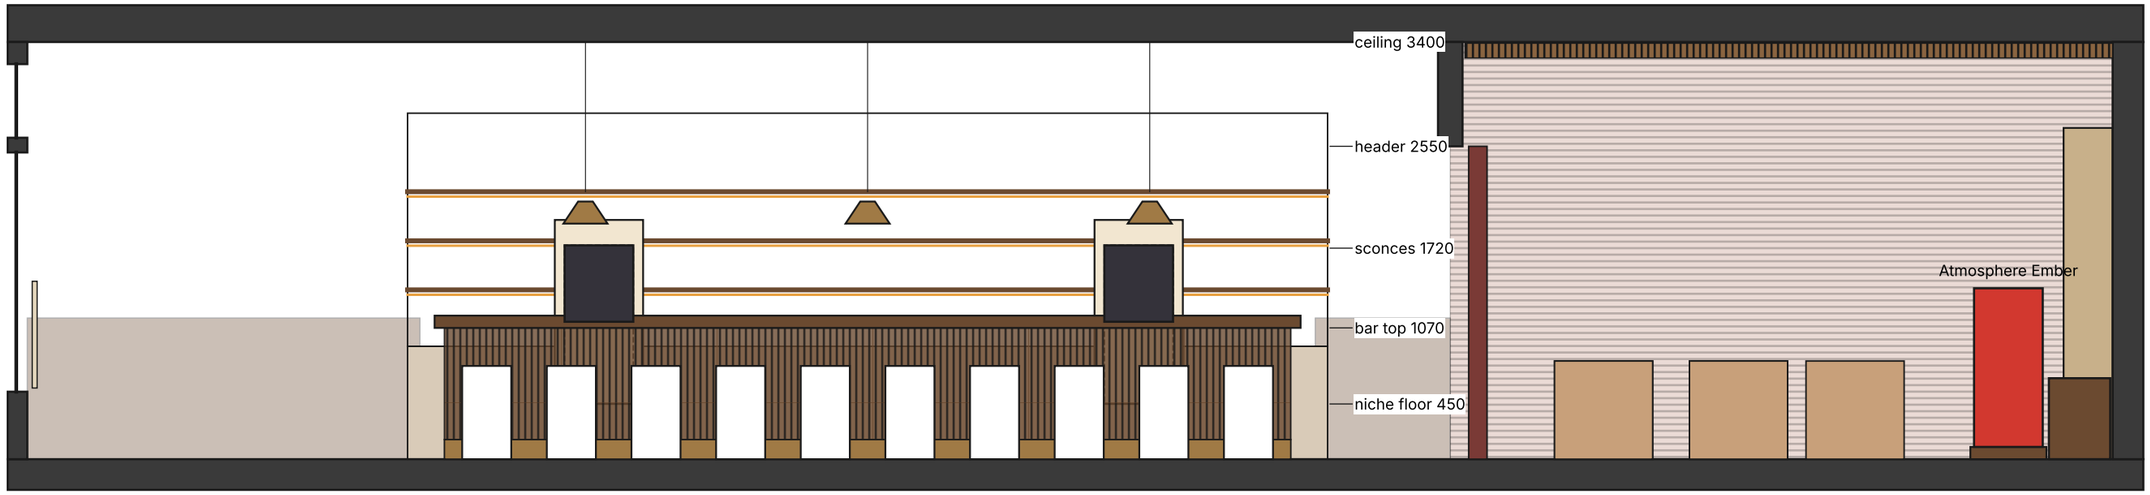

Light, by source, all warm (2200 to 2700 K) and in pools: sconces, the bar's three pendants, the back-bar's shelf strips and niche pinholes, Bell and candles on the tables, the record wall's picture light, a soft lamp over each Ember speaker. No coloured light but the speakers' own.

Long section A-A

Planet EARF: Listening bar, San Francisco (a proposal, round 33)

mm | issue 2026-10-19 | first angle

Set out from the shell's inside faces; joinery to +-2, the shell +-10

PLE-002 rev B