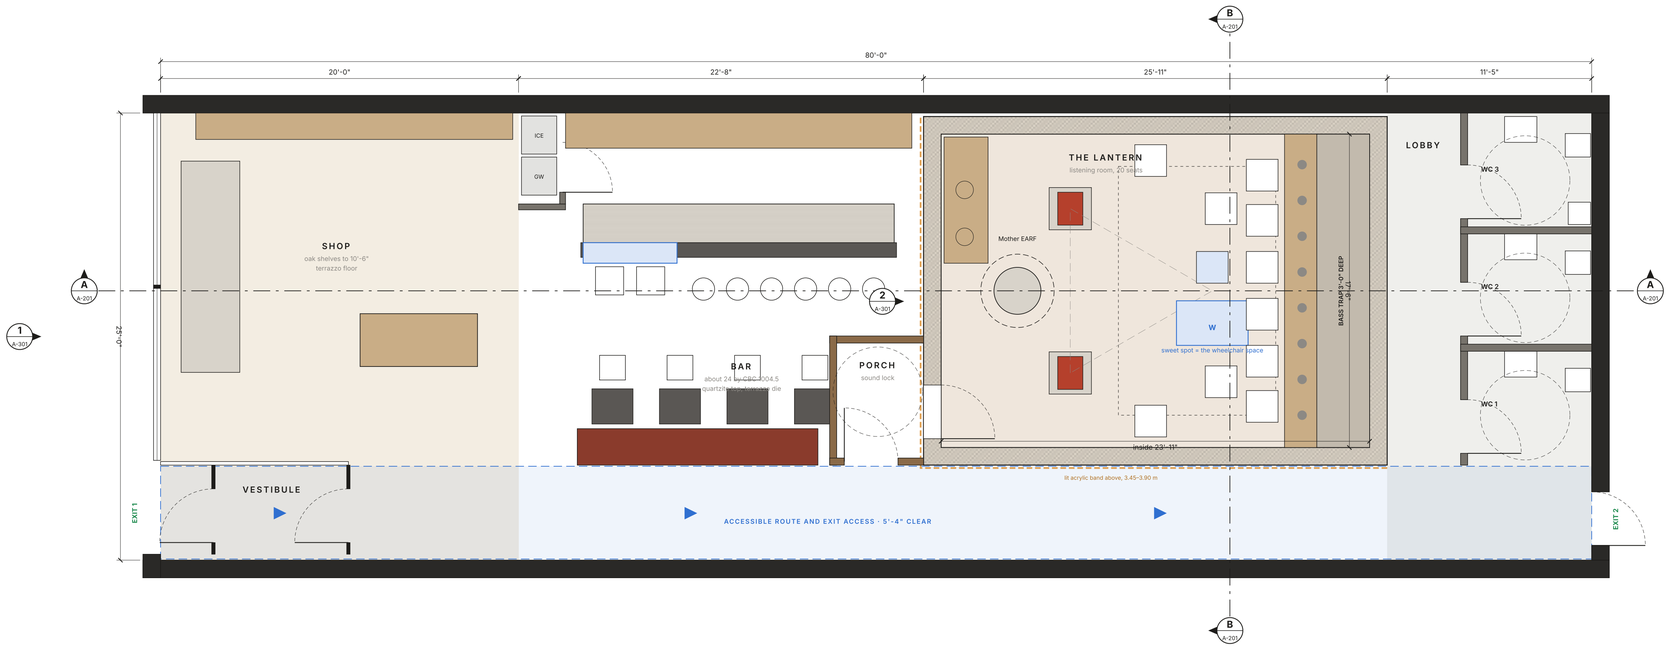


1. Two exits (CBC 1006.2.1: over 49 occupants): the front door and the rear door, 24 m apart, joined by one straight route 5'-4" clear (ADA 403; 60 in to pass and turn). The lantern holds 20, under 50: one door.
2. Posted load about 53 by CBC Table 1004.5 (shop 60 gross; bar 15 net; the lantern by its seats). Under 100, so CBC 903.2.1.2 does not require sprinklers for the A-2 by its load; the building may still have them.
3. The lantern stands free: a 60 mm gap to the party wall, a 60 mm gap to the ceiling, its floor a 100 mm slab on spring mounts (about 7 Hz) in a 175 mm cut in the existing slab, so it finishes flush: no step.
4. The ice machine and the glasswasher sit in a gasketed alcove at the shop end of the back bar, 6.5 m from the lantern's face. Restroom plumbing stays outside the box.
5. The wheelchair space (30 × 48 in, with its companion seat) is on the sweet spot, row 1, floor level: ADA 221.2.1.1 asks one for 4 to 25 seats; 221.2.3.2 Exc. 1 waives vertical dispersion under 300.
6. Three single-user all-gender rooms, one with a urinal: CPC Table 422.1 at a load of about 53 asks 3 water closets and 1 urinal (to confirm with DBI). Each holds a 60 in turning circle.
7. The bar's accessible run: 60 in at 34 in (CBC 11B-902.3), at its near end.

PLANET EARF

A listening bar for San Francisco

EARF · earf.world

STATUS

Proposal, not for construction.
Every dimension and choice is a working assumption for the owner to overturn.
Not reviewed by an architect, an engineer or the building official.

SITE (ASSUMED)

A typical San Francisco storefront: 25'-0" x 80'-0" inside the party walls (2,000 sq ft), 14'-0" to the joists of the flats above, a slab on grade, a glazed front and a rear yard.
No site chosen: the scheme is drawn generic and is fitted to the lease.

THE IDEA

The listening room's isolation, a room within the room, is the building's one object: an oak box on its own floated floor, lit by a band of acrylic fins.

READ WITH

A-102 ceiling and services; A-201 sections; DESIGN.md for the numbers.

SHEETS

A-101	**Floor plan**
A-102	Reflected ceiling plan
A-201	Sections
A-301	Elevations
A-401	Axonometric


ISSUE

Round 44 · the lantern · 31 October 2026 · rev A

Floor plan

1/4" = 1'-0" · 2,000 sq ft · posted load about 53

A-101

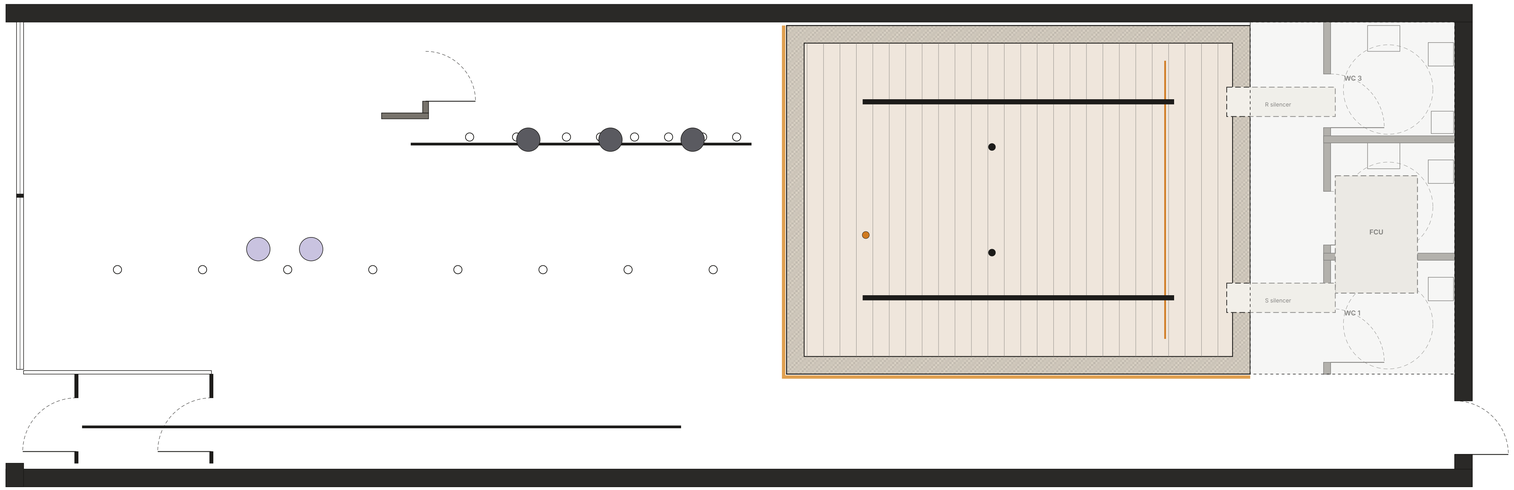

○ downlight, 2700 K, dimmed (the counter, the tables, the shop)
● Hemisphere (the product) over the counter and the shop table
▬ linear slot diffuser (supply), under 2 m/s face velocity
• spot inside the lantern: the pair, Mother EARF (its coloured shadow), the trap's graze
━ the lantern's lit band (amber line), seen from the bar and the route
FCU the lantern's own fan coil on the plant deck; supply and return through lined silencers and flexible connectors at the box's back wall; grilles in the lid at under 1.5 m/s (NC 15–20 target)

1/4" = 1'-0"

0' 4' 8' 16' 32'

PLANET EARF

A listening bar for San Francisco

EARF · earf.world

STATUS

Proposal, not for construction.
Every dimension and choice is a working assumption for the owner to overturn.
Not reviewed by an architect, an engineer or the building official.

SITE (ASSUMED)

A typical San Francisco storefront:
25'-0" x 80'-0" inside the party walls (2,000 sq ft), 14'-0" to the joists of the flats above, a slab on grade, a glazed front and a rear yard.
No site chosen: the scheme is drawn generic and is fitted to the lease.

CEILINGS

Shop and bar: 13'-0", acoustic plaster on resilient clips under the joists (a second line to the flats), 12 in plenum.
The lantern's lid: 11'-2" inside, oak slats over wool, carried by its own walls.
Rear rooms: 8'-6"; a plant deck above.

SHEETS

A-101 Floor plan
A-102 Reflected ceiling plan
A-201 Sections
A-301 Elevations
A-401 Axonometric

ISSUE


Round 44 · the lantern · 31 October 2026 · rev A

Reflected ceiling plan

1/4" = 1'-0" · ceilings, light, air


A-102

A LONG SECTION THROUGH THE LANTERN

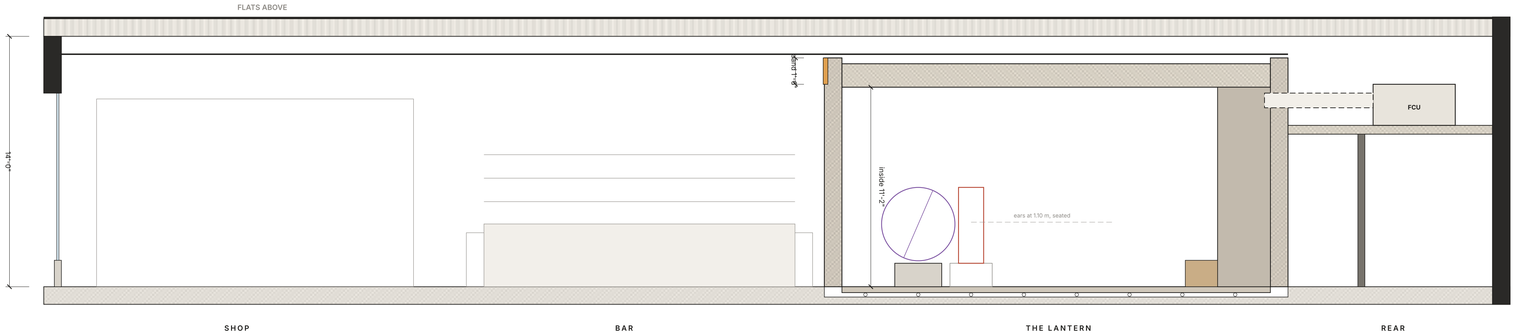

The lantern's wall, outside in: oak skin 20 mm; the band's cavity 60 mm (fins in it, LED and drivers serviced from the route through removable outer fin panels, never through the seal); outer leaf, 2 × 5/8 in gypsum on 3-5/8 in studs; 50 mm air; inner leaf, 2 × 5/8 in gypsum on 2-1/2 in studs with 50 mm wool; oak slats inside.
The lid: CLT 200 + 2 × 5/8 in gypsum + 100 mm wool + oak slats, spanning wall to wall, never hung from the joists.
The floor: 100 mm concrete on spring jack-up mounts (about 7 Hz), end-grain oak on top, in a 175 mm cut.
Every service enters through a flexible connector; the two doors are gasketed sets with drop seals.
Demountable: the oak, the leaves and the lid are bolted panels, numbered, so the box can leave with the lease.

B CROSS SECTION AT THE SWEET SPOT

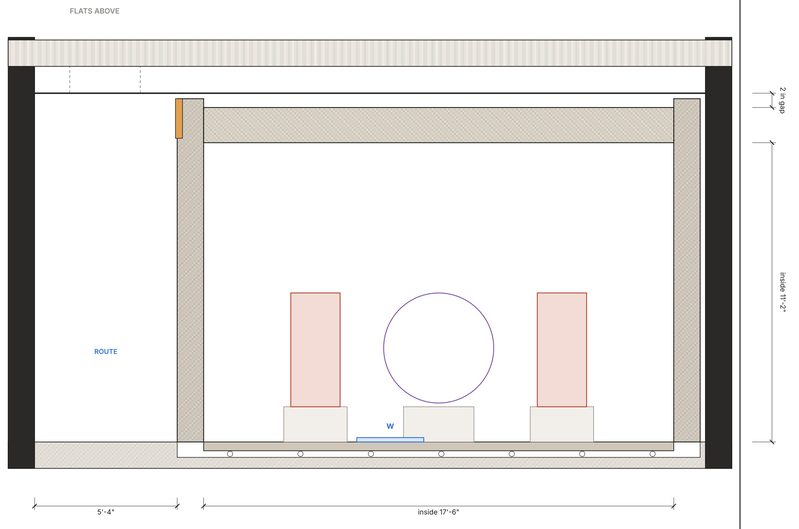

PLANET EARF

A listening bar for San Francisco

EARF · earf.world

STATUS

Proposal, not for construction.
Every dimension and choice is a working assumption for the owner to overturn.
Not reviewed by an architect, an engineer or the building official.

SITE (ASSUMED)

A typical San Francisco storefront:
25'-0" x 80'-0" inside the party walls (2,000 sq ft), 14'-0" to the joists of the flats above, a slab on grade, a glazed front and a rear yard.
No site chosen: the scheme is drawn generic and is fitted to the lease.

ISOLATION

Box in box: the lantern's floor, walls and lid touch the building only through its springs. Targets for the acoustician: music in the flats under 45 dBC at night (Police Code 2909, ambient floor 45 dBC); NC 15-20 inside the box.

SHEETS

A-101 Floor plan
A-102 Reflected ceiling plan
A-201 Sections
A-301 Elevations
A-401 Axonometric

ISSUE

Round 44 · the lantern · 31 October 2026 · rev A

Sections


A long, 1/4" = 1'-0" · B across, 3/8" = 1'-0"

A-201

1 THE STREET



2 THE LANTERN FROM THE BAR

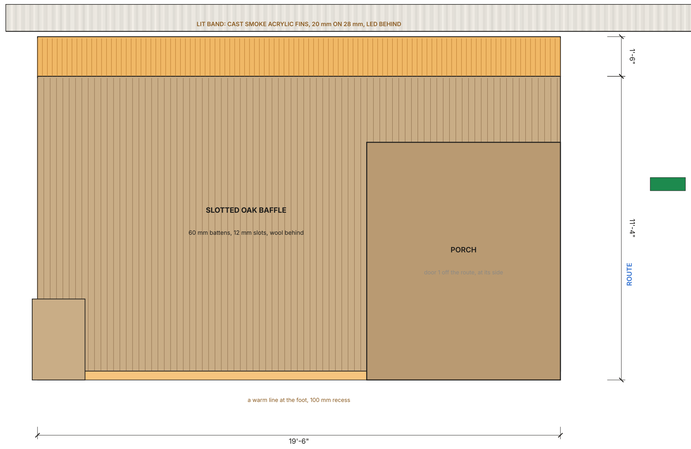

PLANET EARF

A listening bar for San Francisco

EARF · earf.world

STATUS

Proposal, not for construction.
Every dimension and choice is a working assumption for the owner to overturn.
Not reviewed by an architect, an engineer or the building official.

SITE (ASSUMED)

A typical San Francisco storefront:
25'-0" x 80'-0" inside the party walls (2,000 sq ft), 14'-0" to the joists of the flats above, a slab on grade, a glazed front and a rear yard.
No site chosen: the scheme is drawn generic and is fitted to the lease.

MATERIALS

Floors: honed epoxy terrazzo (marble and glass chips); end-grain oak inside the lantern.
Bar top: honed quartzite. Die and plinths: terrazzo with 15% acrylic offcut chips (no wear there).
Oak: oiled white oak, fumed a shade.
Acrylic: the band only, behind the oak line.

SHEETS

A-101 Floor plan
A-102 Reflected ceiling plan
A-201 Sections
A-301 Elevations
A-401 Axonometric

ISSUE

Round 44 · the lantern · 31 October 2026 · rev A

Elevations

3/8" = 1'-0" · 1 the street · 2 the lantern from the bar

A-301