Floor plan, 1:50. Metres in the plan; dimensions in millimetres. North is up the page only as drawn (the long street at the bottom, the side street at the left). A proposal: every number is a working assumption (README, "Assumptions") for the owner to overturn.

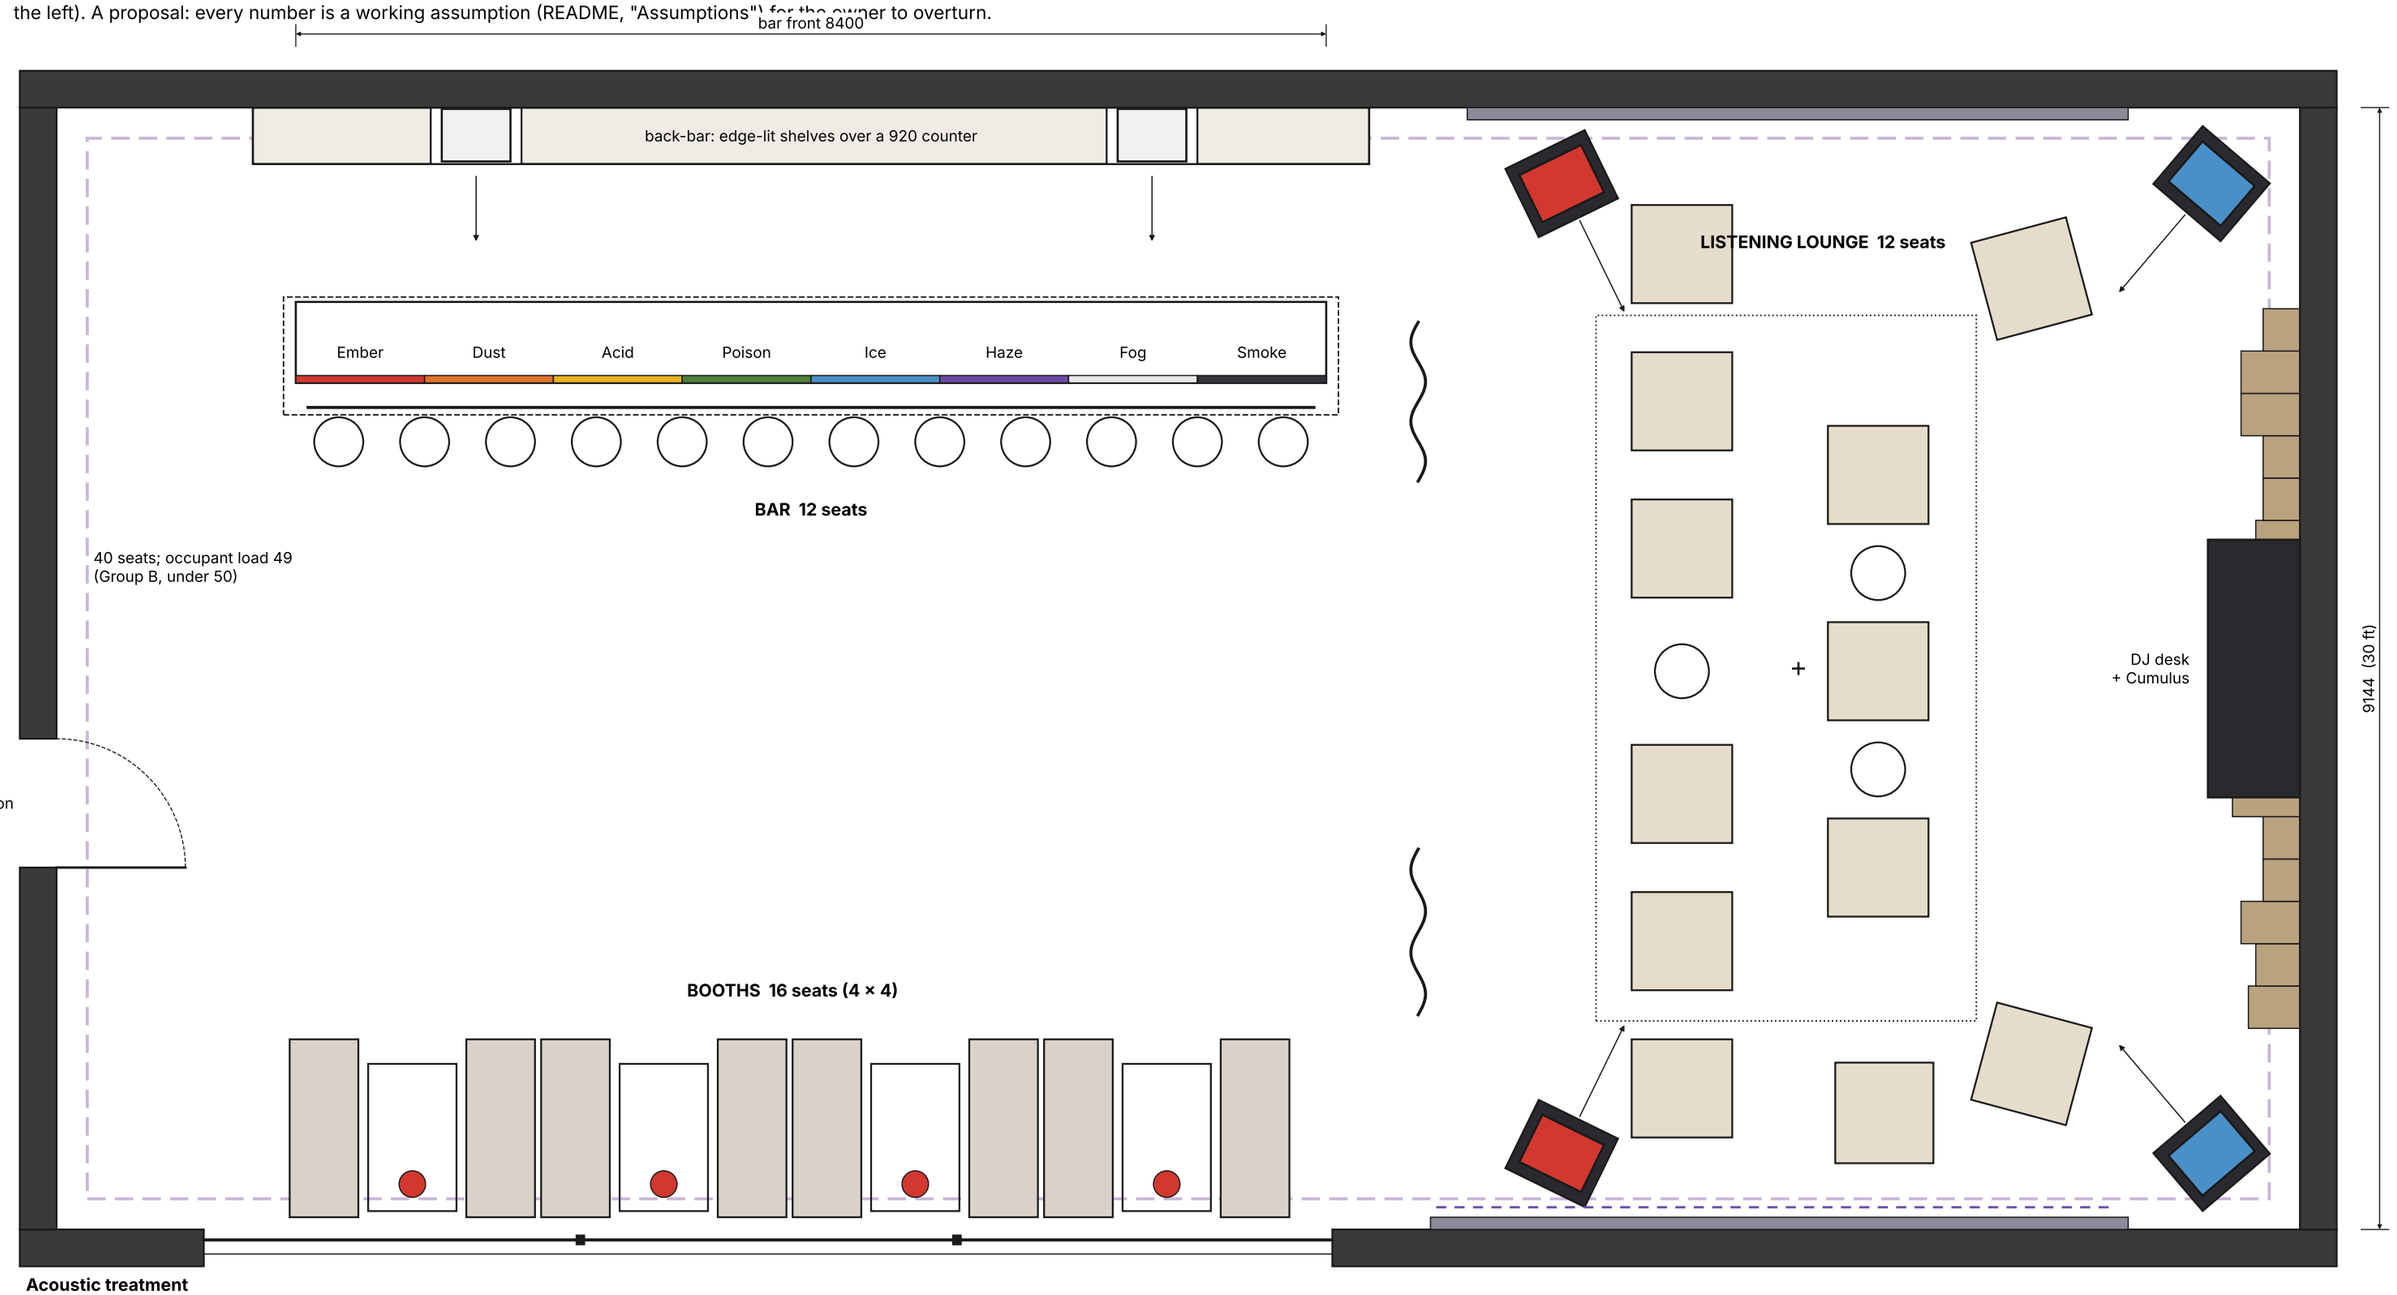

Acoustic treatment

- ceiling: back-lit micro-perforated membrane, 570 plenum with absorber (NRC 0.85), dashed
- tinted Haze slats 75 × 12 at 150, 75 proud of the absorber (street wall of the lounge)
- dark fabric-faced absorber, 100 (both lounge side walls)
- record wall: cubbies 300 to 550 deep, a diffuser

Products

Atmosphere pairs on Smoke plinths 120 high: Ember (the lounge's front corners), Ice (either side of the record wall); arrows: each speaker's axis, aimed at the listening seat (+). The Fog pair: the back-bar's niches, floor 450. Bell: six Fog pendants over the bar, four Ember lamps on the booth tables. Cumulus (Ice): the DJ desk.

Floor plan

Planet EARF: Listening bar, Hayes Valley, San Francisco (a proposal)

mm | issue 2026-10-18 | first angle

Set out from the shell's inside faces; built to +-5, panels and shelves +-1

Long section A-A, 1:50, cut along the room 5500 from the street wall, looking at the party wall: what is cut is drawn heavy, what lies beyond it light. Heights in millimetres above the finished floor.

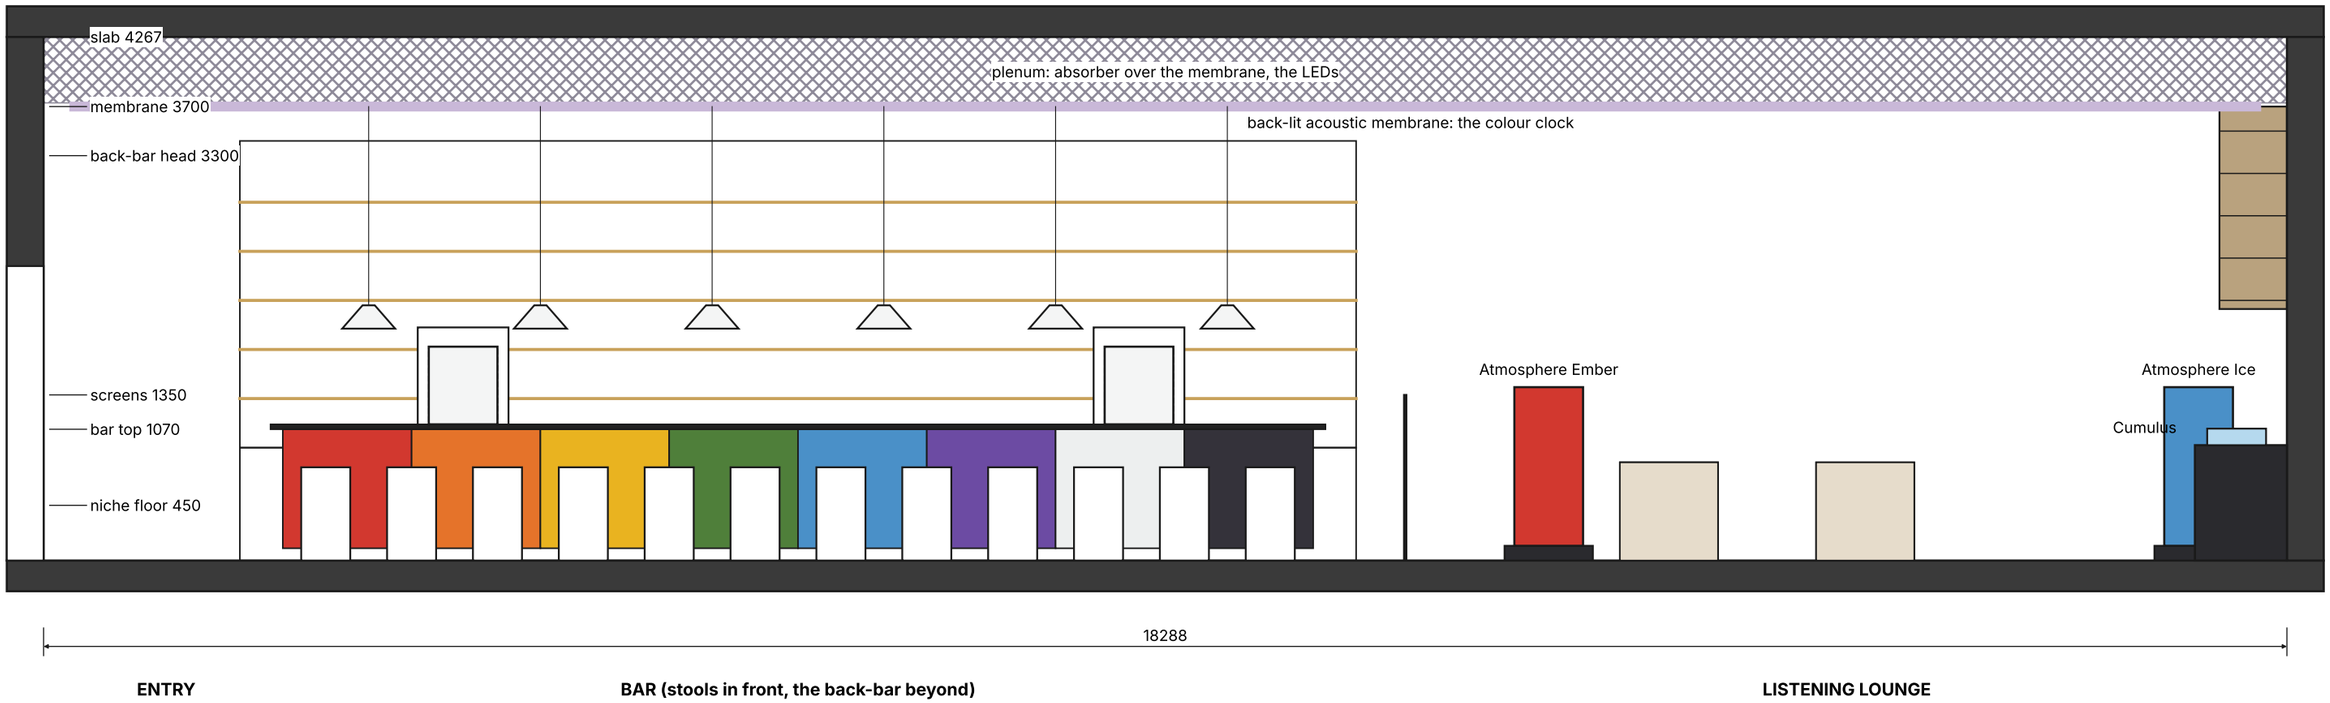

Light, by source: the membrane (the colour clock); the bar's eight panels, back-lit through a white liner from LEDs in a 75 cavity; the back-bar's light-guide shelves and Fog-white back panel; the niches; the slats' LED in their gap; Bell; pinhole spots on each corner pair, the bar top and the DJ desk. Section cut drawn heavy; beyond, light.

Long section A-A

Planet EARF: Listening bar, Hayes Valley, San Francisco (a proposal)

mm | issue 2026-10-18 | first angle

Set out from the shell's inside faces; built to +-5, panels and shelves +-1