PLANET EARF

A listening bar for San Francisco. One floor, 2,800 sq ft, 55 seats.

The shop and the window lounge at the street; the bar room under Mother EARF; the selector in a wall of records; the listening room behind it, its Tropos stacks facing the front.

KEY PLAN · 1/8" = 1'-0"





AREAS

Shop and window lounge	850 sq ft
Bar room, the booth, the record wall	988 sq ft
Listening room and lobby	528 sq ft
Back of house: three WCs, stock and office, the corridor	415 sq ft
Partitions and the lobby walls	20 sq ft
Inside the walls	**2,800 sq ft**

OCCUPANT LOAD · CBC 2022 TABLE 1004.5

Shop (mercantile)	230 sf	/ 60 gross	**4**
Window lounge (tables and chairs)	530 sf	/ 15 net	**36**
Bar room (tables and chairs)	694 sf	/ 15 net	**47**
Banquette (fixed seating)	57 sf	by seat	**12**
Behind the bar and the booth (commercial kitchen)	196 sf	/ 200 gross	**1**
Listening room (tables and chairs)	479 sf	/ 15 net	**32**
Stock and office	87 sf	/ 150 gross	**1**
Occupant load			**133**

Seats 55 · standing room at the counter and the shop. Post the load at the door (CBC 1004.9).

OPTION: 87 OCCUPANTS, NO SPRINKLER REQUIREMENT

Count the front room as the shop it is (mercantile, 60 sq ft gross a person: 15) and fix the listening chairs to the floor (11 seats): 87 in all. Ask the building official before relying on it.

WHAT THE LOAD TRIGGERS (CALIFORNIA BUILDING AND PLUMBING CODES, 2022; SF AMENDMENTS)

Group	A-2 (a bar, 50 or more). Under 50 it would be a B, with no Place of Assembly permit: not possible at this size and seat count.
Exits	Two (more than 49): the street door and the rear door, a third of the diagonal apart (sprinklered). Doors swing out with panic hardware.
Sprinklers	Required for A-2 at 100 or more (CBC 903.2.1.2). Check the building: many SF shells have them; else a deferred submittal.
Fire alarm	Not required for A-2 under 300 (CBC 907.2.1). Emergency lights and lit exit signs are.
Place of Assembly	SF Fire Department permit for 50 or more, with the load posted.
Egress width	0.2 in per occupant for doors (sprinklered): 27 in needed, 32 in clear at each door.
Plumbing	CPC Table 422.1 for A-2; three single-user all-gender WCs, each accessible, counted for either sex (CPC 422.2). Confirm the count against the plumbing official's load.
Accessibility	CBC 11B: one level, 36 in routes, the counter's 60 in low end at 34 in, 5% of dining seats accessible, accessible WCs.
Energy	Title 24 Part 6 lighting allowance for the space types; dimming and controls throughout.

All proposals. The building official sets the load; an architect and the city's plan check confirm every line before anything is built. Sources and the permit path: spinoffs/barkhorn/planet/r42/RULES.md.

PLANET EARF

A listening bar for San Francisco

EARF · earf.world

STATUS

Proposal, not for construction.
Every dimension and choice is a working assumption for the owner to overturn.
Not reviewed by an architect, an engineer or the building official.

SITE (ASSUMED)

A ground floor 35'-0" x 80'-0" inside the walls: 2,800 sq ft. Existing shell, 15'-9" to the joists, one street front, a rear yard with a side passage to the street. No site chosen.

SHEETS

A-000	**The house in numbers**
A-101	Floor plan
A-102	Reflected ceiling plan
A-201	Sections
A-301	Axonometric
A-401	The pop-up


ISSUE

Round 42 · 31 October 2026 · rev A

The house in numbers

areas, load, code

A-000

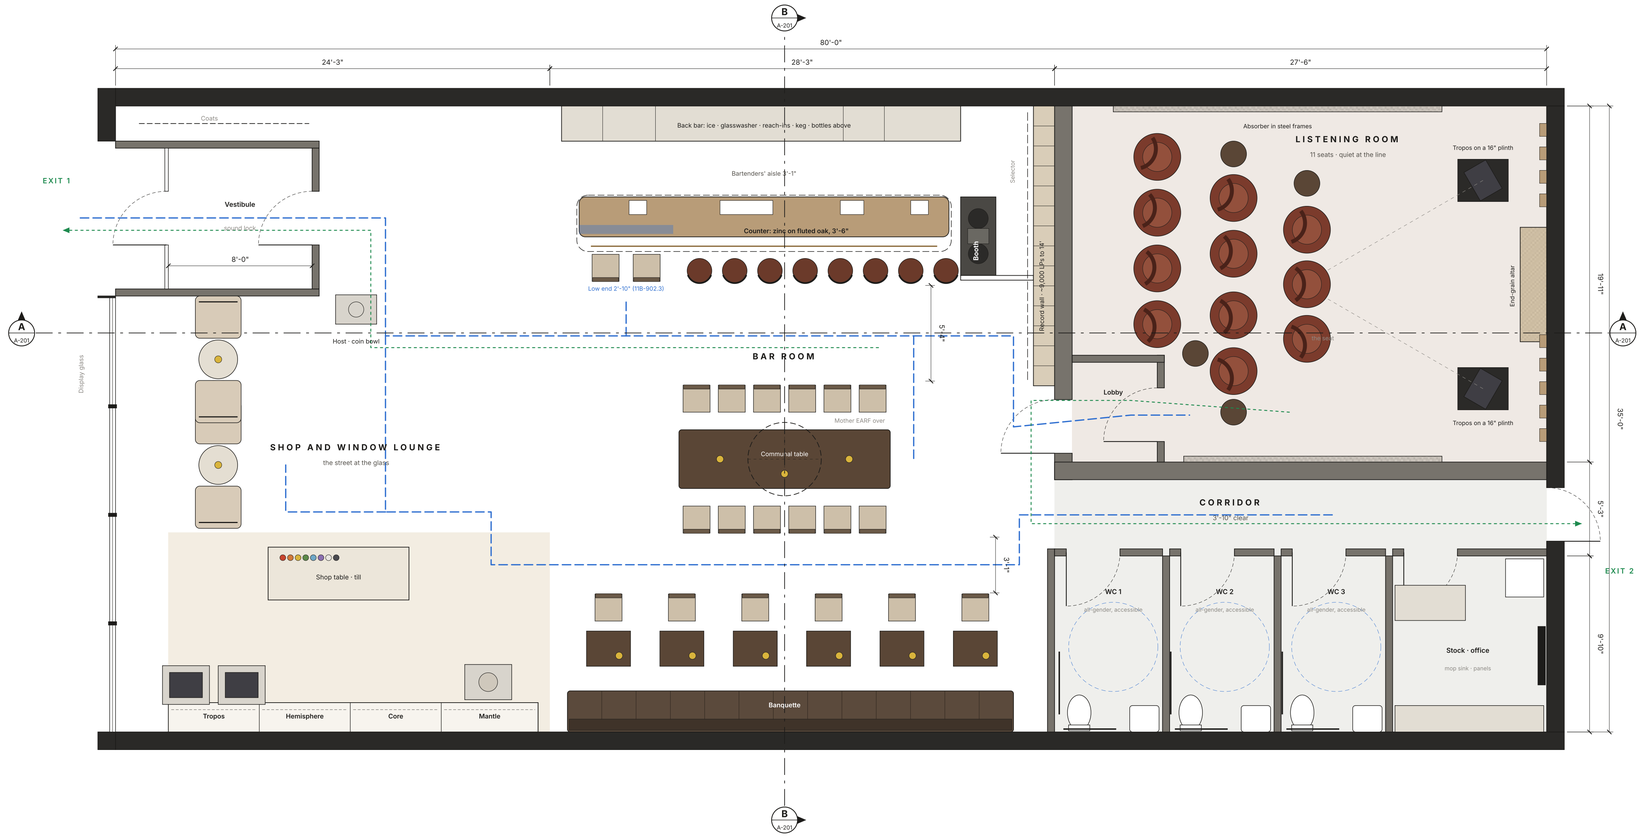

LEGEND

- Existing walls (assumed)
- New partitions; the listening room double stud
- Accessible route (36 in min; 44 in on the main aisle)
- Exit path; two exits, panic hardware
- Core on the table
- Tropos
- Above: the counter top, Mother EARF

SEATS

Window lounge	4
Counter (8 high, 2 at the low end)	10
Banquette and its tables	18
Communal table	12
Listening room	11
Seats in all	**55**

OCCUPANT LOAD (CBC TABLE 1004.5)

Shop (mercantile)	230 sf	/ 60 gross	4
Window lounge (tables and chairs)	530 sf	/ 15 net	36
Bar room (tables and chairs)	694 sf	/ 15 net	47
Banquette (fixed seating)	57 sf	by seat	12
Behind the bar and the booth (commercial kitchen)	196 sf	/ 200 gross	1
Listening room (tables and chairs)	479 sf	/ 15 net	32
Stock and office	87 sf	/ 150 gross	1
Occupant load: Group A-2, sprinklered (100 and over)			**133**

PLAN NOTES

1. The shell is assumed: an existing concrete or masonry ground floor, sprinklered or able to be. A site visit decides it.
2. Two exits for an occupant load over 49 (CBC 1006.2): the street door through the vestibule and the rear door to the yard and side passage, more than a third of the diagonal apart (sprinklered). Both swing outward with panic hardware (CBC 1010.2.9).
3. The vestibule is a sound lock: two doors in series 8 ft apart, felt-lined, so the line stays inside when guests come and go (Police Code Art. 29).
4. The listening room is a room within the room: double-stud walls on isolated clips, its own ceiling at 12 ft, a lobby with two doors. Its stacks face the front, away from the party walls.
5. Accessible: one level throughout, 36 in routes, 44 in on the main aisle; the counter drops to 34 in for its first 5 ft 3 in (CBC 11B-902.3); 5% of table seats at 30 in (11B-226); three single-user all-gender WCs, each with a 60 in turning circle.
6. Behind the bar: a hand sink at each end, a three-compartment sink and a dump sink in the underbar; ice, a glasswasher, reach-ins and a keg box under the back bar (DPH plan check).
7. Everything on the floor is on sale: each piece carries a card. The shop wall holds stock and the pieces not in use.

PLANET EARF

A listening bar for San Francisco

EARF · earf.world

STATUS

Proposal, not for construction.
Every dimension and choice is a working assumption for the owner to overturn.
Not reviewed by an architect, an engineer or the building official.

SITE (ASSUMED)

A ground floor 35'-0" x 80'-0" inside the walls: 2,800 sq ft. Existing shell, 15'-9" to the joists, one street front, a rear yard with a side passage to the street. No site chosen.

READ WITH

A-000 for the occupant load and the code thresholds; A-102 for the lamps.

SHEETS

A-000	The house in numbers
A-101	**Floor plan**
A-102	Reflected ceiling plan
A-201	Sections
A-301	Axonometric
A-401	The pop-up


ISSUE

Round 42 · 31 October 2026 · rev A

Floor plan

1/4" = 1'-0" · 2,800 sq ft · 55 seats

A-101

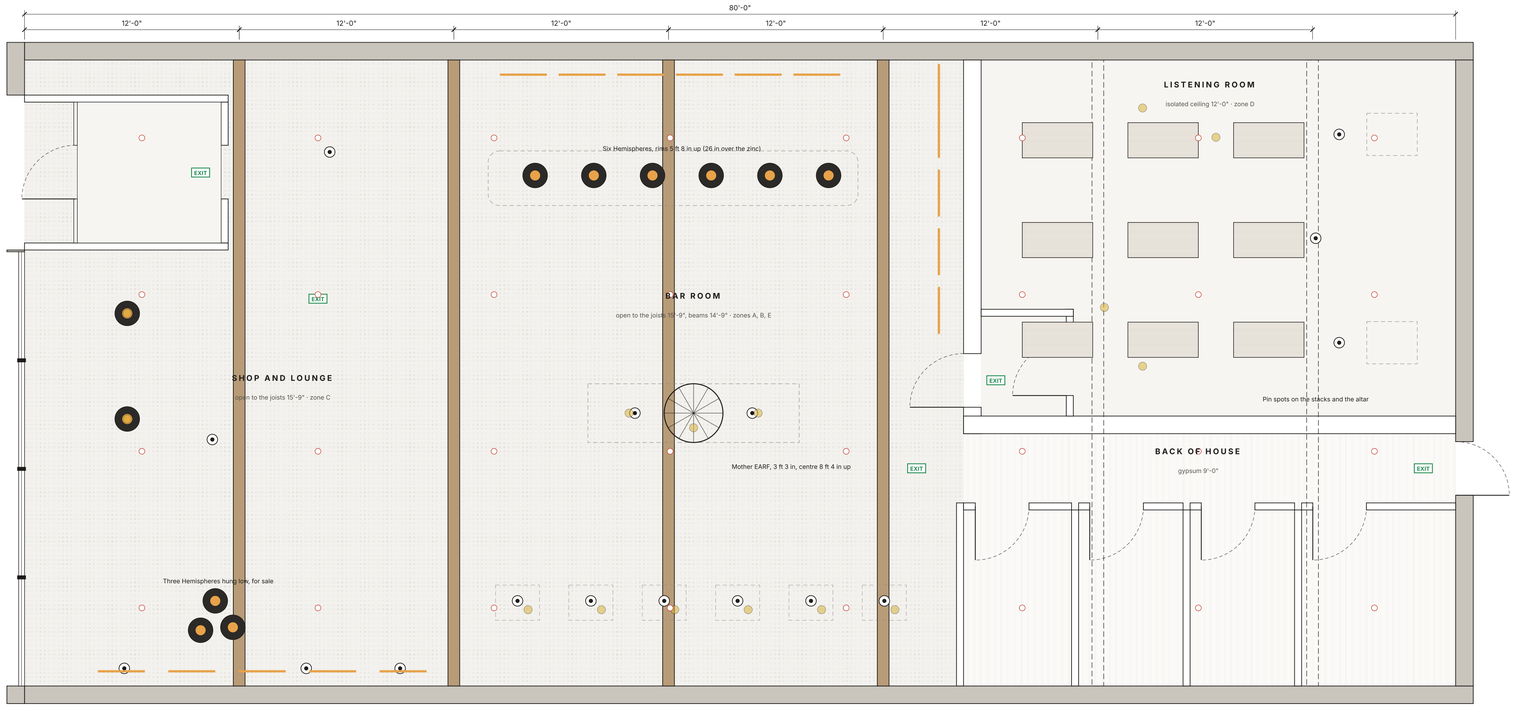

1/4" = 1'-0"

0' 4' 8' 16' 32'

LEGEND

- Hemisphere, pendant: 575 lm, 2700 K, dimmed; rim 26 in over the counter
- Mother EARF: the 1 m globe in multicolour, hung from the joists, its own spot
- Adjustable spot, 2700 K, 15 to 25 degrees, on a ceiling track or the beams
- Linear LED in the shelves: the back bar, the shop wall, the record wall
- Core, on the tables (for reference: not on the ceiling)
- EXIT — Exit sign, with the emergency lights on its circuit
- Sprinkler head, pendent: schematic, by the fire protection contractor
- Acoustic cloud, 2 in mineral wool in fabric, hung 12 in under the listening ceiling

LAMP SCHEDULE

Hemisphere	counter, shop, lounge	**11**	A, C
Mother EARF	over the communal table	**1**	E
Spots	tables, stacks, altar, shop	**16**	B, C, D
Core	every table, the shop	**15**	on the table
Linear LED	shelves (ft)	**60**	A, C
Exit signs	battery-backed	**5**	life safety

Zones: A counter · B tables · C shop and lounge · D listening · E Mother EARF

Load: about 0.5 W per sq ft in the public rooms (Title 24 allows about 1.0 for a bar).

PLANET EARF

A listening bar for San Francisco

EARF · earf.world

STATUS

Proposal, not for construction.
Every dimension and choice is a working assumption for the owner to overturn.
Not reviewed by an architect, an engineer or the building official.

SITE (ASSUMED)

A ground floor 35'-0" x 80'-0" inside the walls: 2,800 sq ft. Existing shell, 15'-9" to the joists, one street front, a rear yard with a side passage to the street. No site chosen.

LIGHT

Warm and low: 2700 K everywhere, 2200 K on the dimmed Hemispheres late. No light source visible from a seat. Five dimming zones on one scene controller (the colour clock).

CEILINGS

Bar and shop: open to the joists, the fir beams exposed, spray acoustic cellulose on the deck between them, black (NRC 0.75 to 0.95 at 1 in).
Listening room: isolated gypsum on clips at 12 ft, clouds under it.
Back of house: gypsum at 9 ft.

SHEETS

A-000 The house in numbers
A-101 Floor plan
A-102 Reflected ceiling plan
A-201 Sections
A-301 Axonometric
A-401 The pop-up

ISSUE

Round 42 · 31 October 2026 · rev A

Reflected ceiling plan

1/4" = 1'-0" · lamps and ceilings

A-102

A · SECTION ALONG THE HOUSE, LOOKING AT THE LEFT WALL

1/4" = 1'-0" · cut at 22'-4" from the right wall (A-101)




1/4" = 1'-0"

0' 4' 8' 16' 32'

B · SECTION ACROSS THE BAR ROOM, LOOKING TOWARD THE BACK

3/8" = 1'-0" · cut through the communal table and Mother EARF (A-101)

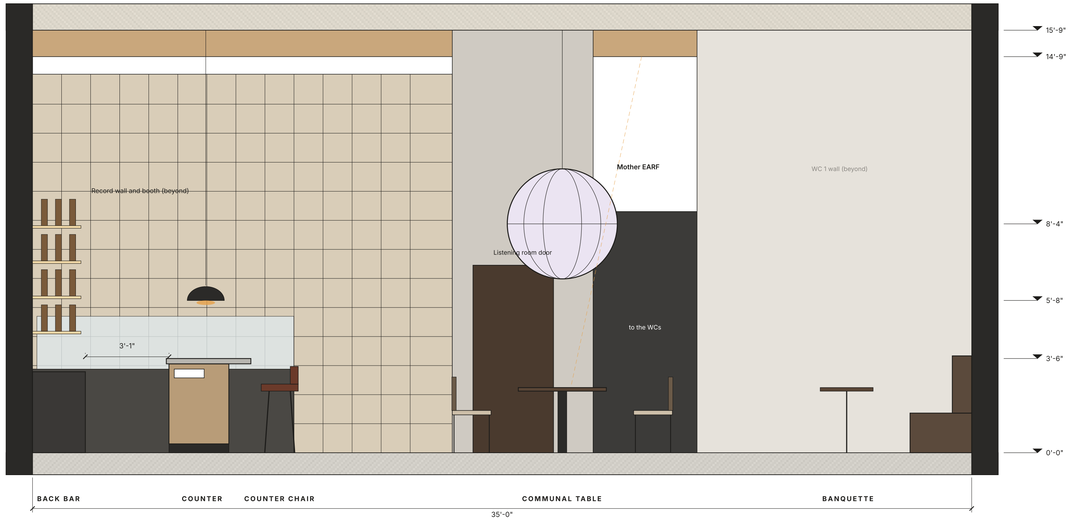

3/8" = 1'-0"

0' 4' 8' 16' 32'

PLANET EARF

A listening bar for San Francisco

EARF · earf.world

STATUS

Proposal, not for construction.
Every dimension and choice is a working assumption for the owner to overturn.
Not reviewed by an architect, an engineer or the building official.

SITE (ASSUMED)

A ground floor 35'-0" x 80'-0" inside the walls: 2,800 sq ft. Existing shell, 15'-9" to the joists, one street front, a rear yard with a side passage to the street. No site chosen.

HEIGHTS

Floor 0'-0" · counter 3'-6" · low end 2'-10" · Hemisphere rims 5'-8" · Mother EARF 8'-4" · listening ceiling 12'-0" · beams 14'-9" · joists 15'-9"

SOUND

The stacks fire toward the front, on mass-loaded plinths on the slab; the listening room floats on its own walls and ceiling, 2 layers of gypsum each side, insulation between (STC 60+).

SHEETS

A-000 The house in numbers
A-101 Floor plan
A-102 Reflected ceiling plan
A-201 **Sections**
A-301 Axonometric
A-401 The pop-up

ISSUE

Round 42 · 31 October 2026 · rev A

Sections

A at 1/4", B at 3/8" = 1'-0"

A-201

AXONOMETRIC FROM THE STREET CORNER, THE WALLS CUT AWAY



1 Vestibule
2 Window lounge
3 Shop wall
4 Back bar
5 Counter
6 Mother EARF
7 Communal table
8 Booth
9 Record wall
10 Banquette
11 Listening room
12 Tropos stacks
13 WCs
14 Altar
15 Rear exit
16 Stock and office

PLANET EARF

A listening bar for San Francisco

EARF · earf.world

STATUS

Proposal, not for construction.
Every dimension and choice is a working assumption for the owner to overturn.
Not reviewed by an architect, an engineer or the building official.

SITE (ASSUMED)

A ground floor 35'-0" x 80'-0" inside the walls: 2,800 sq ft. Existing shell, 15'-9" to the joists, one street front, a rear yard with a side passage to the street. No site chosen.

HOW IT WAS MADE

The plan (plan42.py) built in Blender as a cutaway: the far walls cut at 8 ft 6 in, the near wall at 3 ft 3 in, the back of house at 4 ft 3 in. The products as simple solids in their colours.

SHEETS

A-000 The house in numbers
A-101 Floor plan
A-102 Reflected ceiling plan
A-201 Sections
A-301 Axonometric
A-401 The pop-up


ISSUE

Round 42 · 31 October 2026 · rev A

Axonometric

the plan built as a model

A-301

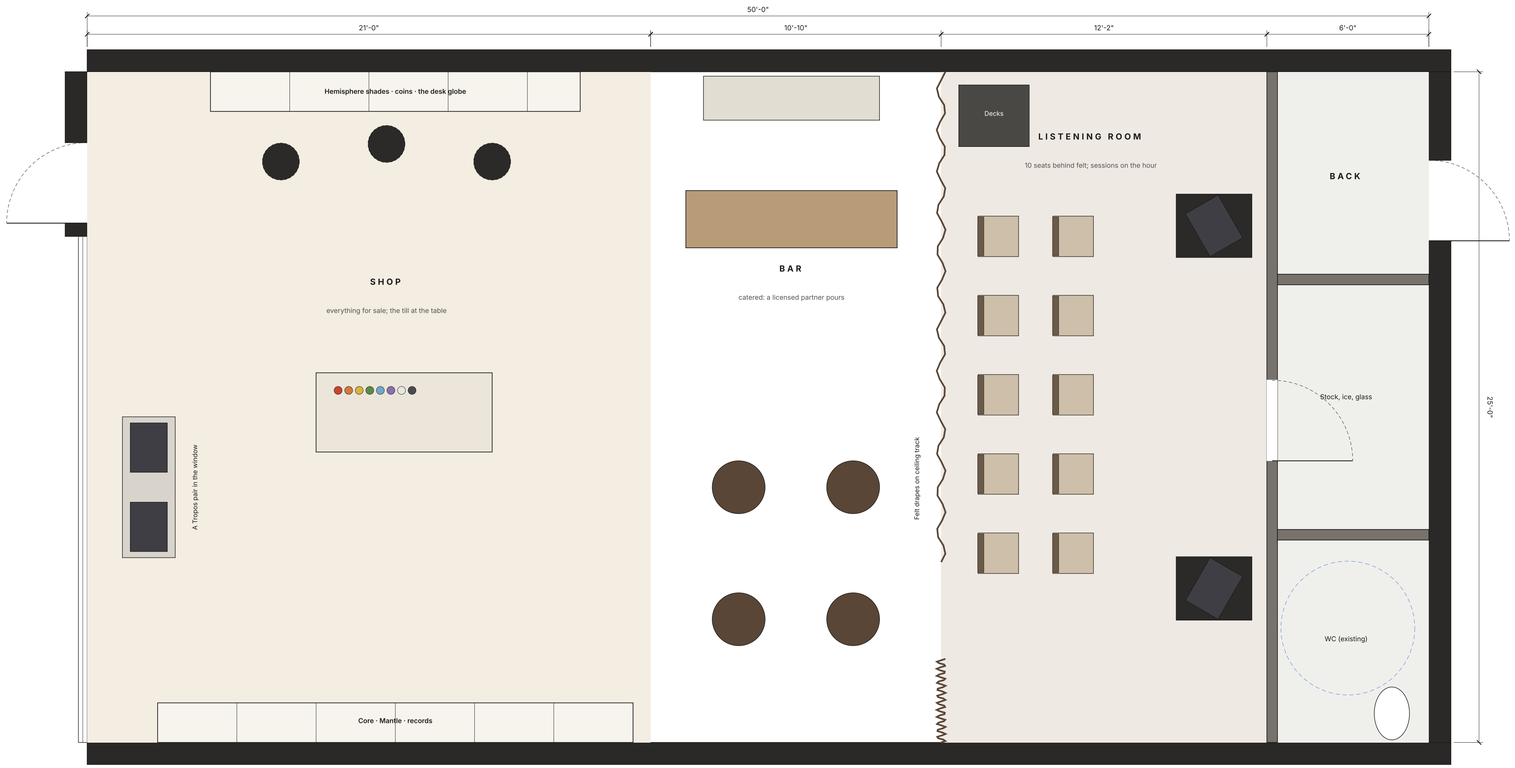

3/8" = 1'-0"

0' 4' 8' 16' 32'

OCCUPANT LOAD

Shop (mercantile, 60 gross)	525 sf	9
Bar and standing tables (15 net, tables)	271 sf	16
Listening room (10 fixed seats)	303 sf	10
Back of house (storage, 300 gross)	151 sf	1
Occupant load: under 50, so no Place of Assembly permit		**36**

WHAT IS BROUGHT IN

Felt drapes on a ceiling track (the listening room), acoustic panels on stands
Two Tropos pairs: one in the window, one on the stacks; amplifiers, decks, 800 records
The shop: shelves on the two walls, the table, 11 Hemispheres and 15 Cores on show and lit
A portable bar with sinks and an ice well, brought by the caterer; rented chairs and tables
Mother EARF? Only if the ceiling can take it: else the 300 mm desk globe in the window

PLANET EARF

A listening bar for San Francisco

EARF · earf.world

STATUS

Proposal, not for construction.
Every dimension and choice is a working assumption for the owner to overturn.
Not reviewed by an architect, an engineer or the building official.

SITE (ASSUMED)

A vacant downtown storefront, 25'-0" x 50'-0": 1,250 sq ft, 13 ft ceiling, an existing accessible WC and a rear door. For 3 to 6 months. No site chosen.

THE BRIDGE

A vacant downtown storefront for 3 to 6 months: the shop, a catered bar and a ten-seat listening room behind felt. Everything portable; nothing built that a short licence cannot carry away.

READ WITH

POPUP.md: the drinks route, the budget, the timeline to FOG week (January 2027) and what it proves.

SHEETS

A-000	The house in numbers
A-101	Floor plan
A-102	Reflected ceiling plan
A-201	Sections
A-301	Axonometric
A-401	**The pop-up**

ISSUE

Round 42 · 31 October 2026 · rev A

The pop-up

3/8" = 1'-0" · 1,250 sq ft · 3 to 6 months

A-401